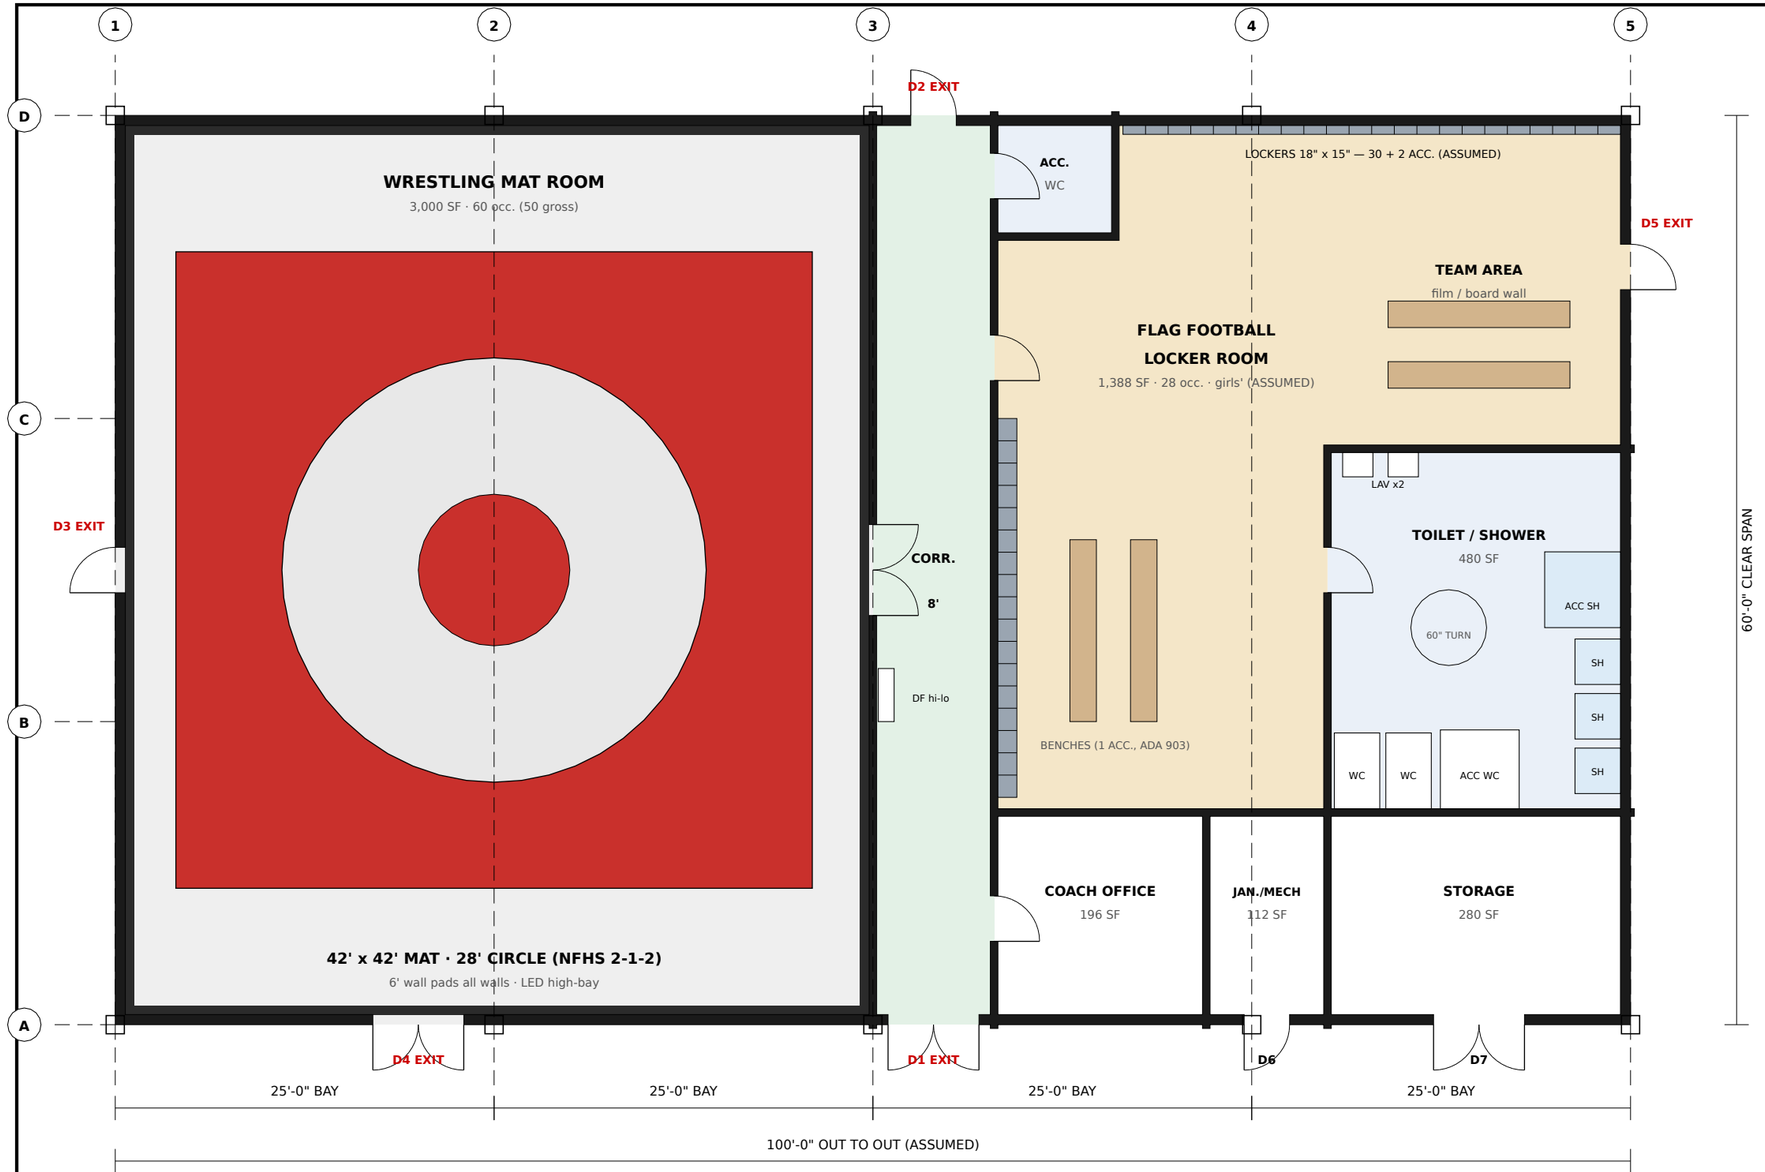

FLOOR PLAN — NEW METAL TRAINING BUILDING (ALTERNATE)

1" = 10'-0" · 100' x 60' = 6,000 SF clear-span PEMB, 4 x 25' bays (ASSUMED) · plan north up

PLAN NOTES

- D-094 (Shane 2026-10-14 9:52 PM CT): new pre-engineered metal building (Summertown Metals) replaces the old 55' x 45' room. West = mat room, east = flag football locker room.
- Size: the 60' x 80' alternate grown to 100' x 60' (ASSUMED) so the locker side holds toilets / showers, office and storage without shrinking the mat room.
- Clear-span rigid frames on lines 1-5 @ 25'; endwall columns @ 20' (A-D). Demising wall on line 3 (frame line). No interior columns.
- Mat room: one 42' x 42' mat (28' circle + 7' each side; NFHS 2-1-2 needs >= 5'). 4' E / W, 9' N / S to the walls; 6' wall pads all walls. Clear 14' min (ASSUMED).
- Locker room: girls' flag football (ASSUMED), 30 lockers + 2 accessible (ADA 222.1, 811), benches (ADA 903), team / film area.
- Toilet / shower: 3 WC (1 acc.), 2 lav, 4 showers (1 acc. roll-in). All-gender accessible single-user toilet off the corridor. DF hi-lo, service sink in JAN. (counts ASSUMED; G-101).
- Exits (red): D1 main pair, D2 north, D3 west, D4 mat-room pair, D5 east. Mat room (60 occ.) has 3 ways out (D3, D4, corridor I1).
- Accessibility: accessible route at grade, 60" turning spaces, 36" doors min; final ADA layout by the architect.
- Wall / interior: insulated metal panels (Summertown kit), 6" interior walls; wet walls TBD (CMU or moisture-resistant). Finishes TBD.
- No prices on this set: cost TBD per the Summertown Metals quote, plus site, foundation, MEP, permit and design (not included).

LEGEND

- wrestling mat (42' x 42')
- 6' wall pads
- locker room
- toilet / shower
- corridor / entry
- lockers

PRELIMINARY — CONCEPTUAL DESIGN — NOT FOR CONSTRUCTION

PROJECT	PHASE	SHEET TITLE	SCALE	DATE	REV	DRAWN BY	SHEET
Hazel Green Regional Athletic Complex **Hazel Green HS · Phase 1 alternate: new metal training building**	**PHASE 1 ALTERNATE**	**FLOOR PLAN** **METAL BUILDING (ALT.)**	**1" = 10'-0"**	**October 2026**	**A**	Drawn by KEYSTONE (AI) for Shane Brazelton	**P1-A-201**